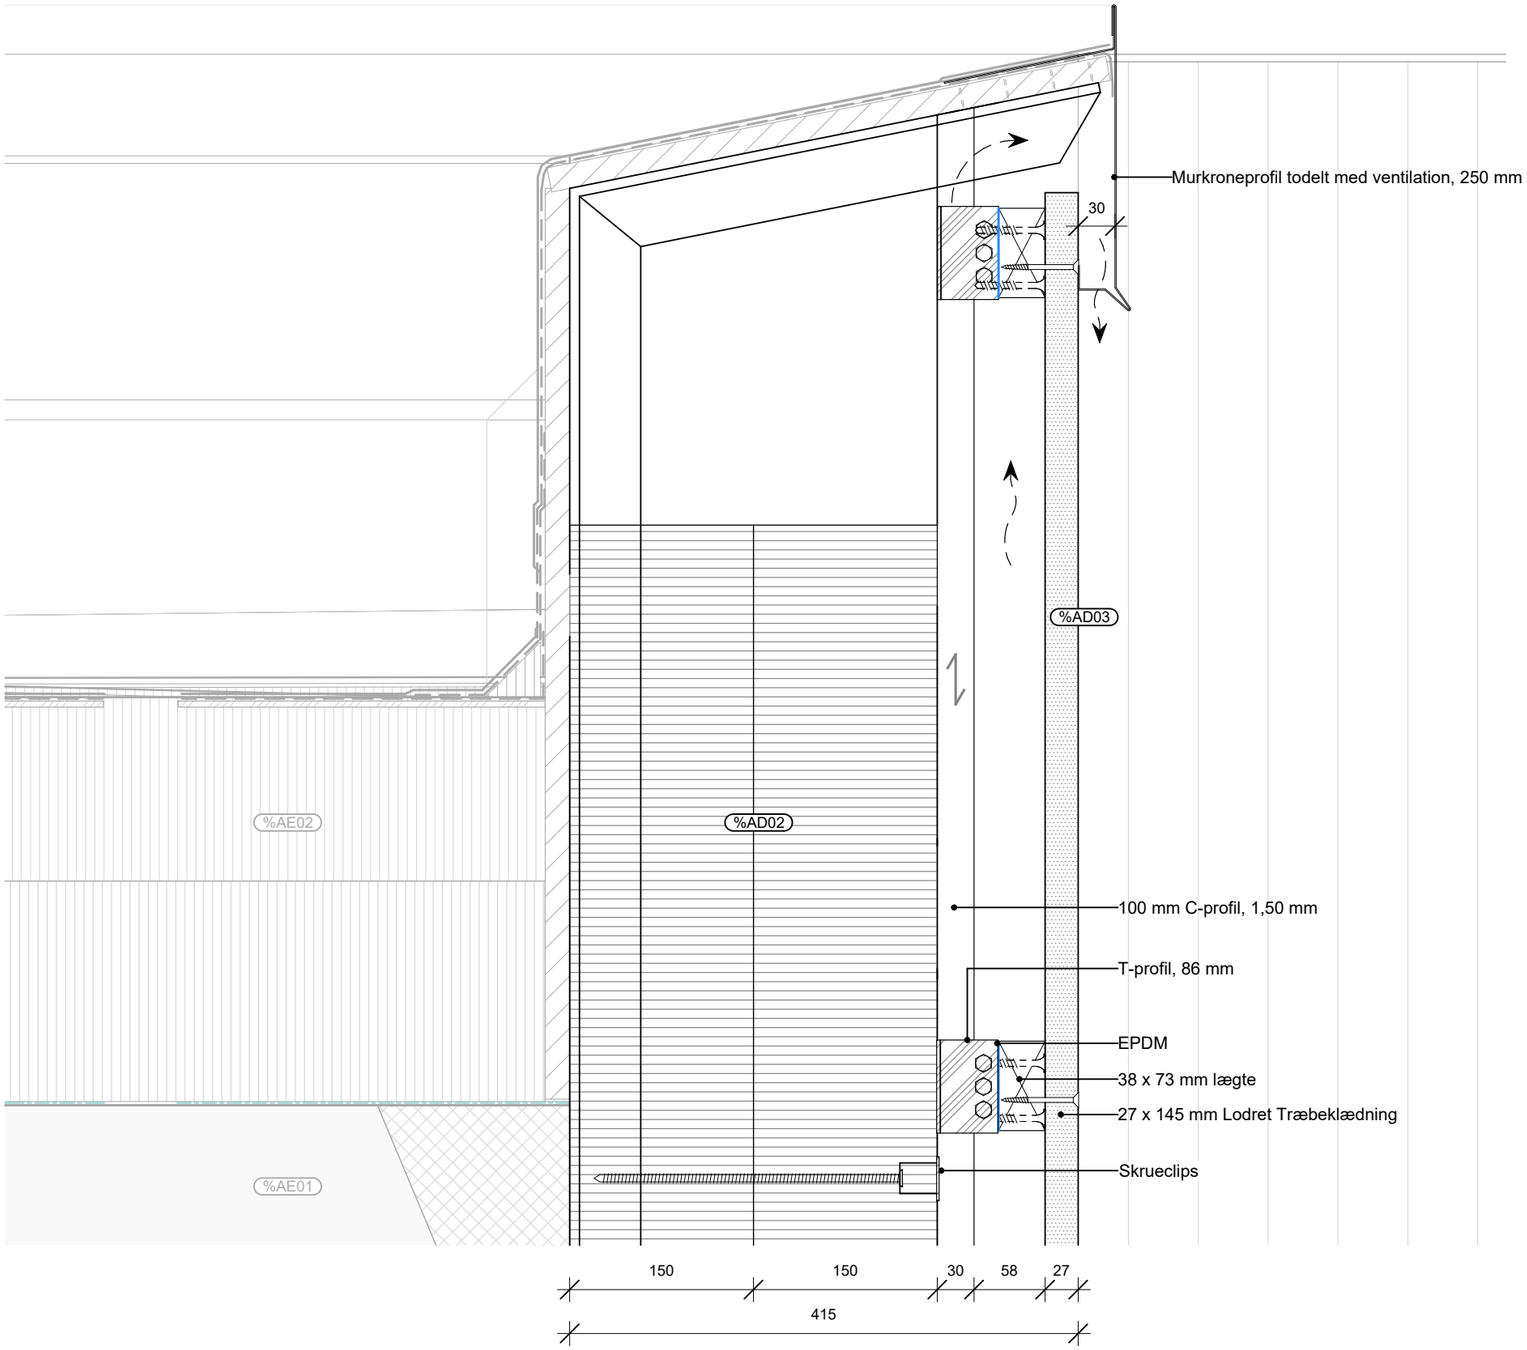


BYGNINGSDELSOVERSIGT

Typekode:	Beskrivelse
%AD02	Ydervæg Isoleringslag 350 mm (0,13 W/m²K) (S215 Skeletkonstruktion) Trykfast og vandafvisende mineraluld 150 mm Trykfast og vandafvisende mineraluld 150 mm Ventileret Stålforskalling 50 mm
%AD03	Ydervæg Træbeklædning 65 mm (S215 Skeletkonstruktion) Træbeklædning 160 mm lodret 27 mm Ventileret Træforskalling 38 x 73 mm C/c 600
%AE01	Huldæk 220 mm (S210 Betonkonstruktion)
%AE02	Tagopbygning Hovedhus 330 - 700 mm (0,09 W/m²K) (S221 Tagdækning) Overpap 4,4 mm Underpap 2,9 mm Skotrendekile Mineraluld, Trykfast og Vandafvisende Kileopbygning Mineraluld, Trykfast og Vandafvisende 1:40 Hældning Isolering Mineraluld, Trykfast og Vandafvisende 150 mm Isolering Mineraluld, Trykfast og Vandafvisende 180 mm Bitumendampspærre 3.1 mm

*Skruer iht. leverandørens anvisninger.

Ny Daginstitution Smørum NDS_A6_K01_H1_EST_N04_S215

Udbudsprojekt

L - Murkrone

Mål: 1 : 5 Dato: 18.06.2026

TS-ARKITEKTER

Sags nr.: NDS Udarbejdet af: ST Kontrol af: TT Godk. af: TS Format: 297 x 420

TS-Arkitekter