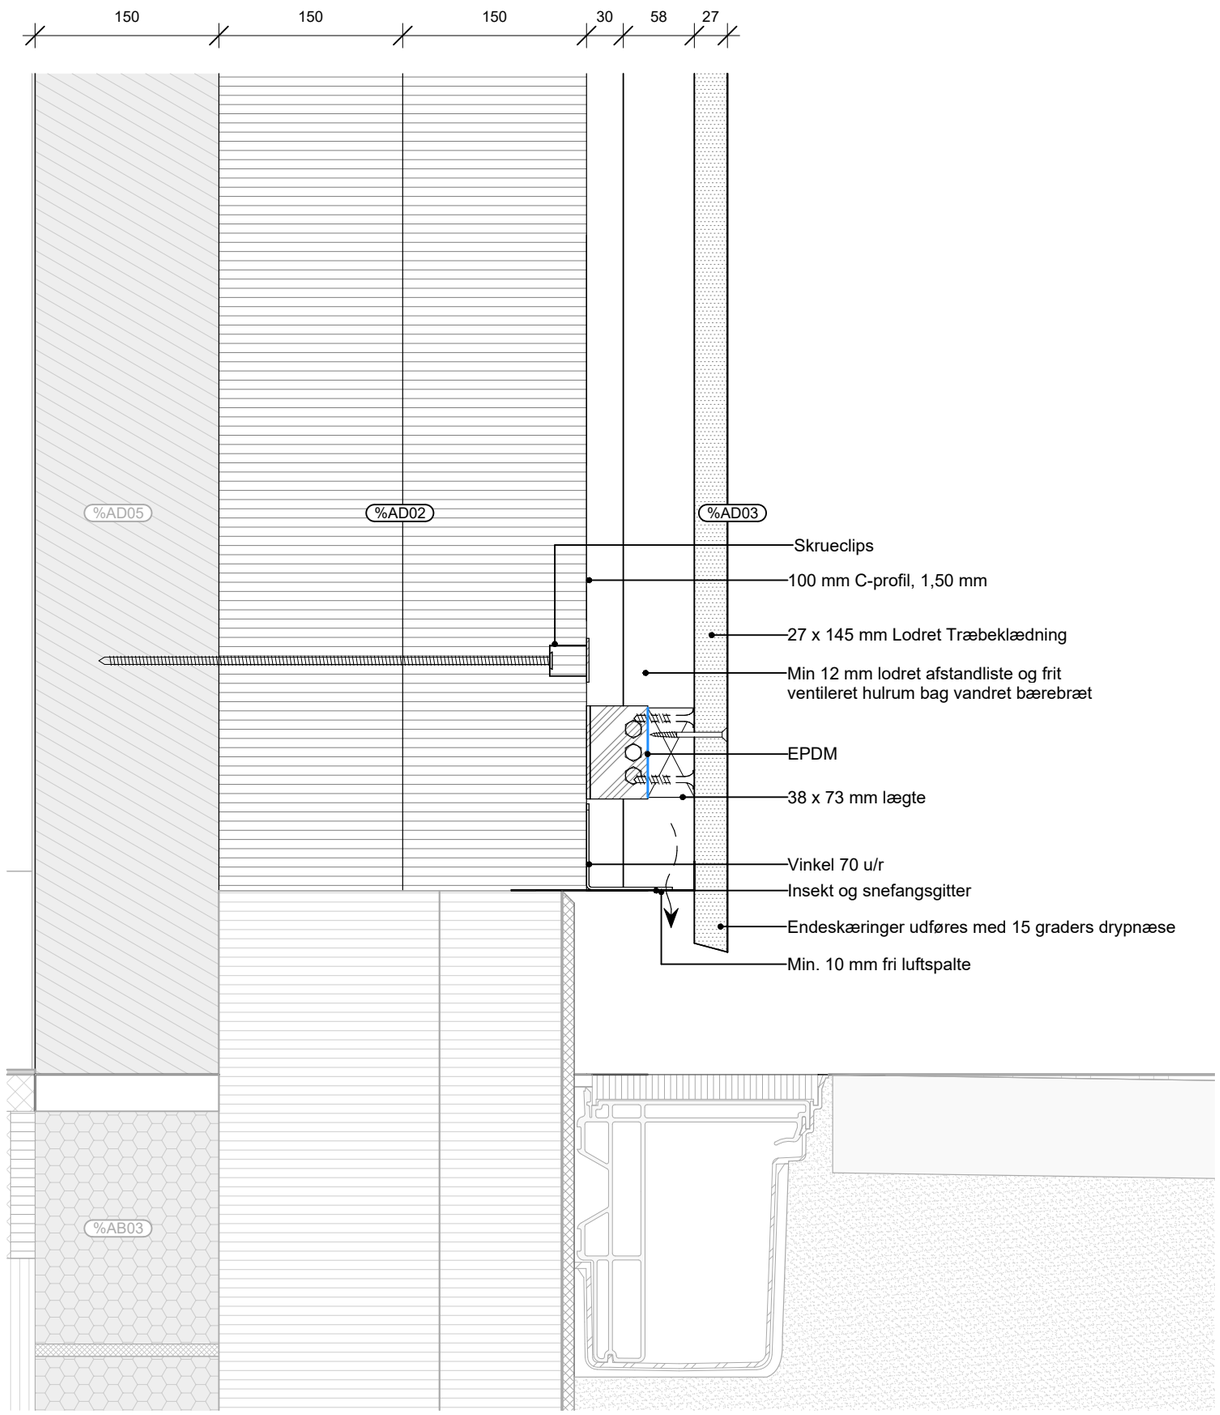


*Skruer iht. leverandørens anvisninger.

BYGNINGSDELSOVERSIGT

Typekode:	Beskrivelse
%AB03	Sokkel 150 mm (S201 Jord) Letbeton, Blokke (Letklinkerblokke) 150 mm
%AD02	Ydervæg Isoleringslag 350 mm (0,13 W/m²K) (S215 Skeletkonstruktion) Trykfast og vandafvisende mineraluld 150 mm Trykfast og vandafvisende mineraluld 150 mm Ventileret Stålforskalling 50 mm
%AD03	Ydervæg Træbeklædning 65 mm (S215 Skeletkonstruktion) Træbeklædning 160 mm lodret 27 mm Ventileret Træforskalling 38 x 73 mm C/c 600
%AD05	Letbeton Bagmur 150 mm (S210 Betonkonstruktion) Letbetonelement 150 mm

Ny Daginstitution Smørum NDS_A6_K01_H1_EST_N03_S215

Udbudsprojekt

L - Væg v. Sokkel

Mål: 1 : 5 Dato: 18.06.2026

TS-ARKITEKTER

Sags nr.: NDS Udarbejdet af: ST Kontrol af: TT Godk. af: TS Format: 297 x 420

TS-Arkitekter