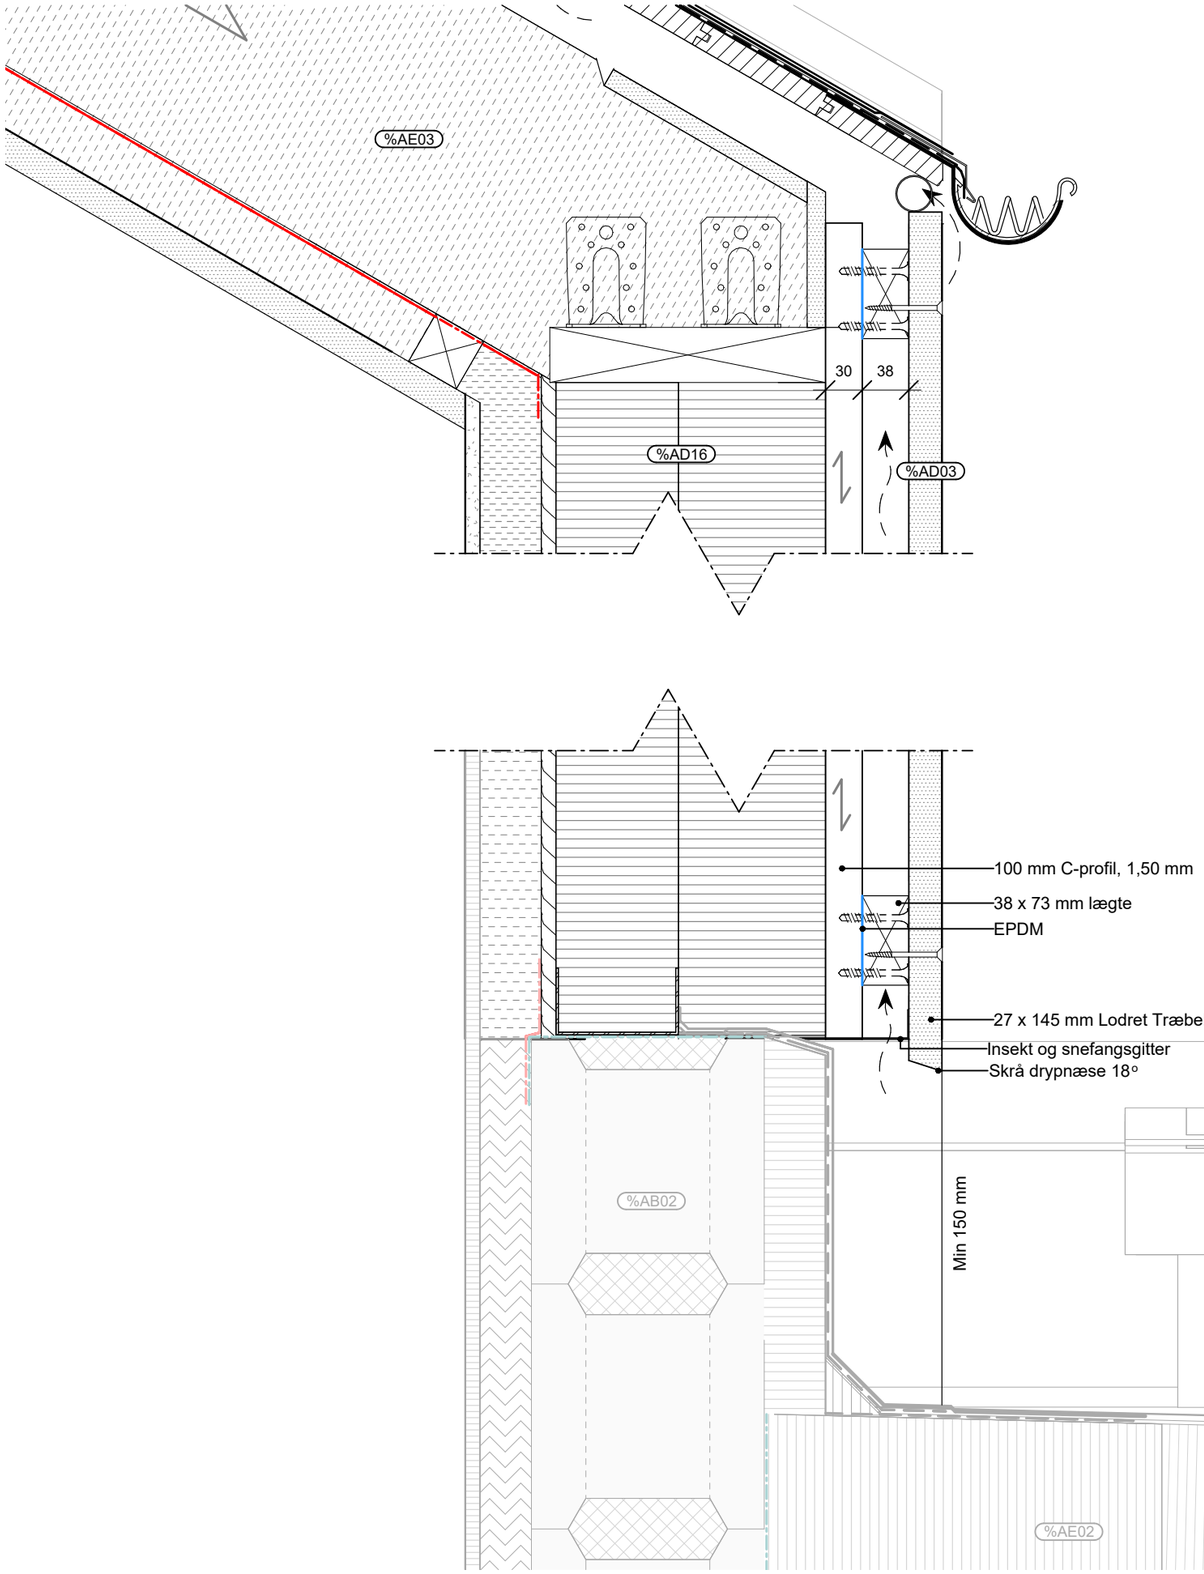


*Skruer iht. leverandørens anvisninger.

BYGNINGSDELSOVERSIGT

Typekode:	Beskrivelse
%AB02	Fundamentsblokke 190 mm (S201 Jord) Indstøbt Betonblokke Med Jern 190 mm
%AD03	Ydervæg Træbeklædning 65 mm (S215 Skeletkonstruktion) Træbeklædning 160 mm lodret 27 mm Ventileret Træforskalling 38 x 73 mm C/c 600
%AD16	Ydervæg Teknikrum 324 mm (0,13 W/m²K) (S215 Skeletkonstruktion) Ventileret Stålforskalling 30 mm Trykfast og vandafvisende mineraluld 120 mm Mineraluld 100 mm OSB 12 mm Installationslag C/c 600 mm 50 mm Fibergips 12 mm
%AE02	Tagopbygning Hovedhus 330 - 700 mm (0,09 W/m²K) (S221 Tagdækning) Overpap 4,4 mm Underpap 2,9 mm Skotrendekile Mineraluld, Trykfast og Vandafvisende Kileopbygning Mineraluld, Trykfast og Vandafvisende 1:40 Hældning Isolering Mineraluld, Trykfast og Vandafvisende 150 mm Isolering Mineraluld, Trykfast og Vandafvisende 180 mm Bitumendampspærre 3.1 mm
%AE03	Tagopbygning Teknikrum - 378 mm (0,12 W/m²K) (S215 Skeletkonstruktion) Rupløjedebrædder 21 mm 95 x 295 mm Spærtræ + kileopbygning med luft 50 mm Mineraluld 245 mm Dampspærre PE 0,20 mm 45 x 45 mm regler med Isolering C/c 600 45 mm Loftbrædder 14 mm
%QQA14	Ovenlysvindue Fællesrum 2000 x 1000 mm (S215 Skeletkonstruktion)

Ny Daginstitution Smørum — NDS_A6_K01_H1_EST_N02_S215

Udbudsprojekt

L - Væg Teknikrum

Mål: 1 : 5 Dato: 18.06.2026

TS-ARKITEKTER

Sags nr.: NDS Udarbejdet af: ST Kontrol af: TT Godk. af: TS Format: 297 x 420

TS-Arkitekter