NDS_A6_K01_H3_EX_N02_S215

BYGNINGSDELSOVERSIGT

Typekode:	Beskrivelse
%AD02	Ydervæg Isoleringslag 350 mm (0,13 W/m²K) (S215 Skeletkonstruktion) Trykfast og vandafvisende mineraluld 150 mm Trykfast og vandafvisende mineraluld 150 mm Ventileret Stålforskalling 50 mm
%AD03	Ydervæg Træbeklædning 65 mm (S215 Skeletkonstruktion) Træbeklædning 160 mm lodret 27 mm Ventileret Træforskalling 38 x 73 mm C/c 600
%AD04	Ydervæg Kompositbeklædning 46 mm (S215 Skeletkonstruktion) Beklædning - Kompositplade 8 mm Ventileret Træforskalling 38 x 73 mm C/c 600
%AD16	Ydervæg Teknikrum 324 mm (0,13 W/m²K) (S215 Skeletkonstruktion) Ventileret Stålforskalling 30 mm Trykfast og vandafvisende mineraluld 120 mm Mineraluld 100 mm OSB 12 mm Installationslag C/c 600 mm 50 mm Fibergips 12 mm
%AE03	Tagopbygning Teknikrum - 378 mm (0,12 W/m²K) (S215 Skeletkonstruktion) Rupløjedebrædder 21 mm 95 x 295 mm Spærtræ + kileopbygning med luft 50 mm Mineraluld 245 mm Dampspærre PE 0,20 mm 45 x 45 mm regler med Isolering C/c 600 45 mm Loftbrædder 14 mm
%BG02	Udendørs Loftbeklædning (S212 Trækonstruktion) Træskelet C/c 600 mm 38 mm Beklædning - Kompositplade 8 mm
%QQA13	Vindue fast 1000 x 1645 mm (S215 Skeletkonstruktion)
%QQC01	Facadedør 1010 x 2145 mm (S215 Skeletkonstruktion)

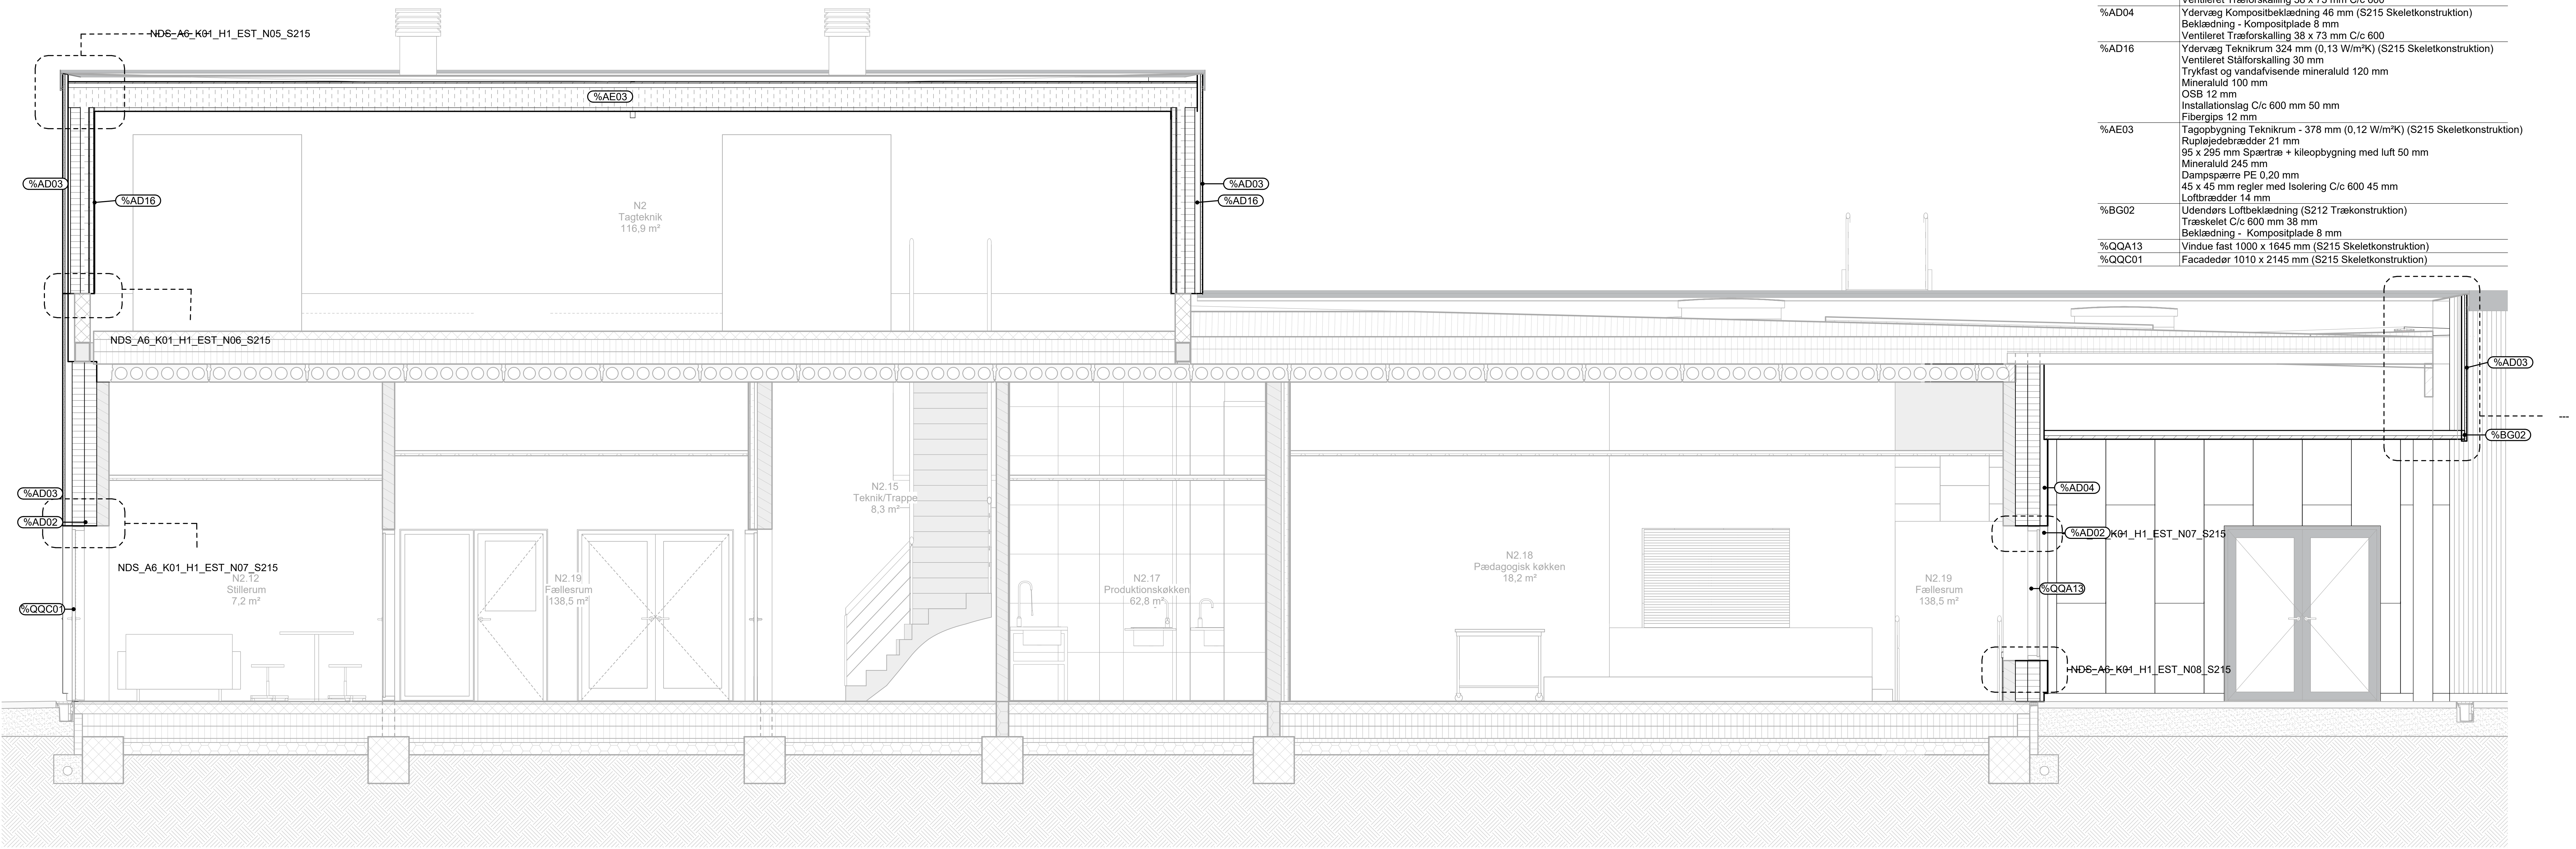

Ny Daginstitution Smørum

NDS_A6_K01_H3_EX_N02_S215

Udbudsprojekt

B-B

Mål: 1 : 50

Dato: 18.06.2026

Sags nr.: NDS

Udarbejdet af: ST

Kontrol af: TT

Godk. af: TS

Format: 297 x 630

● TS-Arkitekter