BYGNINGSDELSOVERSIGT

Typekode:	Beskrivelse
%AD02	Ydervæg Isoleringslag 350 mm (0,13 W/m²K) (S215 Skeletkonstruktion) Trykfast og vandafvisende mineraluld 150 mm Trykfast og vandafvisende mineraluld 150 mm Ventileret Stålforskalling 50 mm
%AD03	Ydervæg Træbeklædning 65 mm (S215 Skeletkonstruktion) Træbeklædning 160 mm lodret 27 mm Ventileret Træforskalling 38 x 73 mm C/c 600
%AD04	Ydervæg Kompositbeklædning 46 mm (S215 Skeletkonstruktion) Beklædning - Kompositplade 8 mm Ventileret Træforskalling 38 x 73 mm C/c 600
%AD16	Ydervæg Teknikrum 324 mm (0,13 W/m²K) (S215 Skeletkonstruktion) Ventileret Stålforskalling 30 mm Trykfast og vandafvisende mineraluld 120 mm Mineraluld 100 mm OSB 12 mm Installationslag C/c 600 mm 50 mm Fibergips 12 mm
%AE03	Tagopbygning Teknikrum - 378 mm (0,12 W/m²K) (S215 Skeletkonstruktion) Rupløjedebrædder 21 mm 95 x 295 mm Spærtræ + kileopbygning med luft 50 mm Mineraluld 245 mm Dampspærre PE 0,20 mm 45 x 45 mm regler med Isolering C/c 600 45 mm Loftbrædder 14 mm
%QQC02	Dobbelt Dør 1910 x 2145 mm (S215 Skeletkonstruktion)

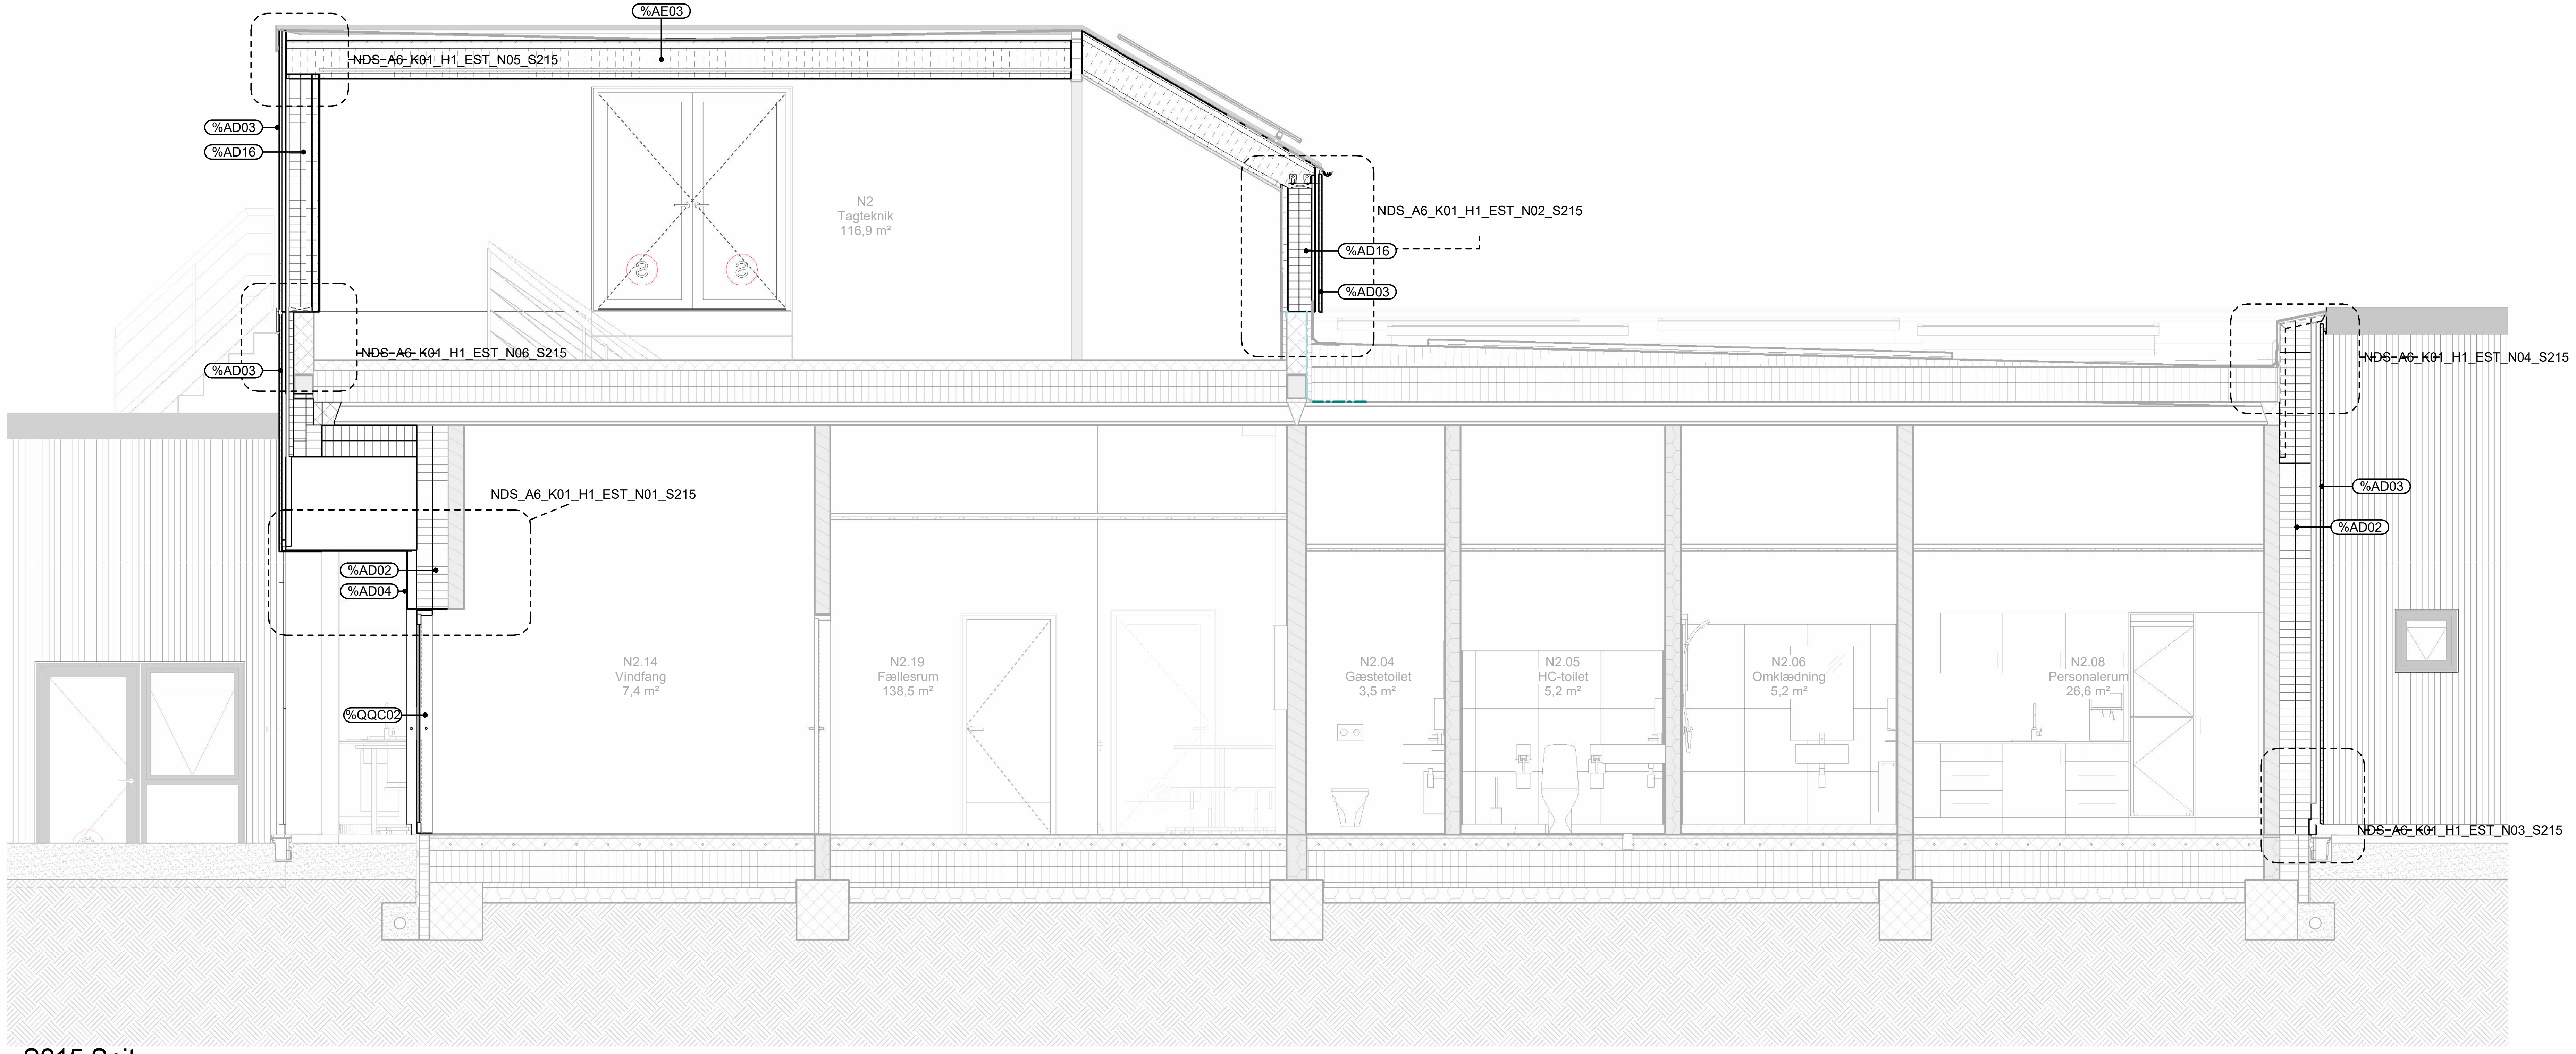
%AE03
NDS_A6_K01_H1_EST_N05_S215
%AD03
%AD16
N2
Tagteknik
116,9 m²
NDS_A6_K01_H1_EST_N02_S215
%AD16
%AD03
NDS_A6_K01_H1_EST_N06_S215
%AD03
NDS_A6_K01_H1_EST_N04_S215
NDS_A6_K01_H1_EST_N01_S215
%AD03
%AD02
%AD02
%AD04
N2.14
Vindfang
7,4 m²
N2.19
Fællesrum
138,5 m²
N2.04
Gæstetoilet
3,5 m²
N2.05
HC-toilet
5,2 m²
N2.06
Omklædning
5,2 m²
N2.08
Personalerum
26,6 m²
%QQC02
NDS_A6_K01_H1_EST_N03_S215

S215 Snit
1 : 50

Ny Daginstitution Smørum
NDS_A6_K01_H3_EX_N01_S215

Udbudsprojekt

A-A

Mål: 1 : 50
Dato: 18.06.2026

TS-ARKITEKTER

Sags nr.: NDS
Udarbejdet af: ST
Kontrol af: TT
Godk. af: TS
Format: 297 x 630

● TS-Arkitekter