

BYGNINGSDELSOVERSIGT


Typekode:	Beskrivelse
%AD03	Ydervæg Træbeklædning 65 mm (S215 Skeletkonstruktion) Træbeklædning 160 mm lodret 27 mm Ventileret Træforskalling 38 x 73 mm C/c 600
%AD04	Ydervæg Kompositbeklædning 46 mm (S215 Skeletkonstruktion) Beklædning - Kompositplade 8 mm Ventileret Træforskalling 38 x 73 mm C/c 600

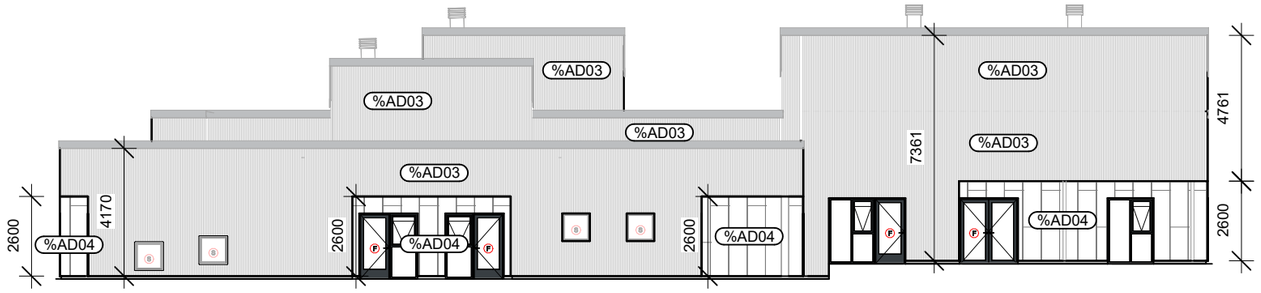


215 - Nord

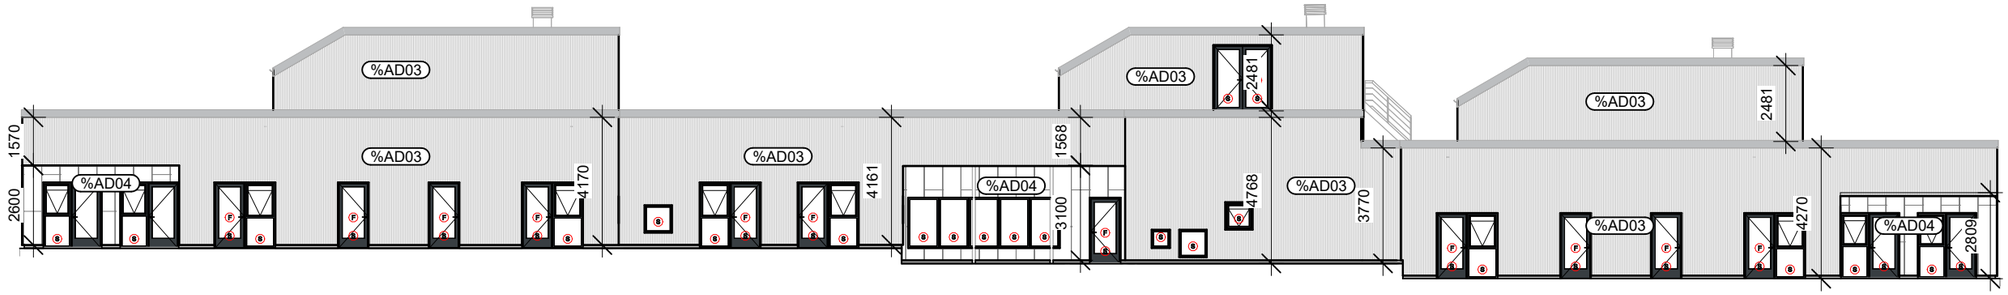

215 - Øst

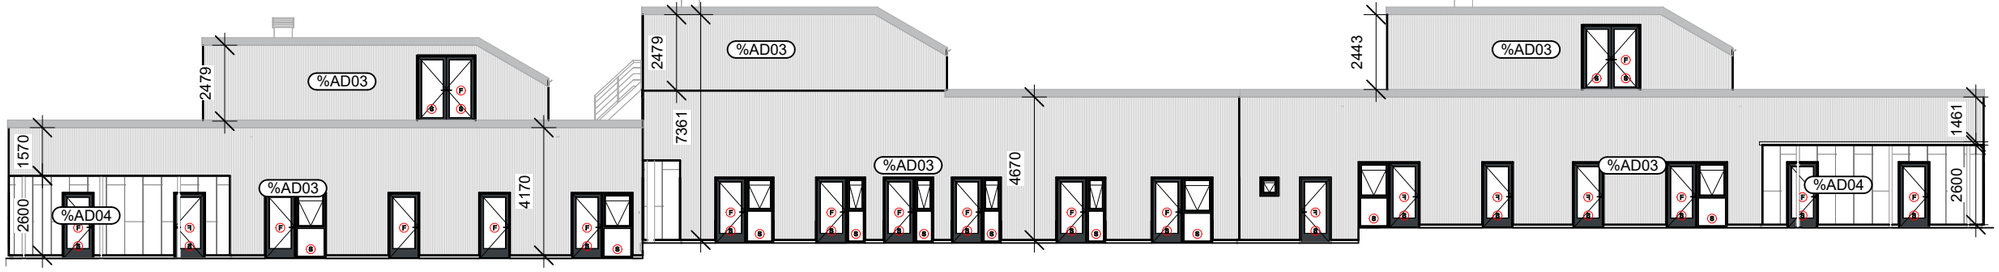

215 - Vest

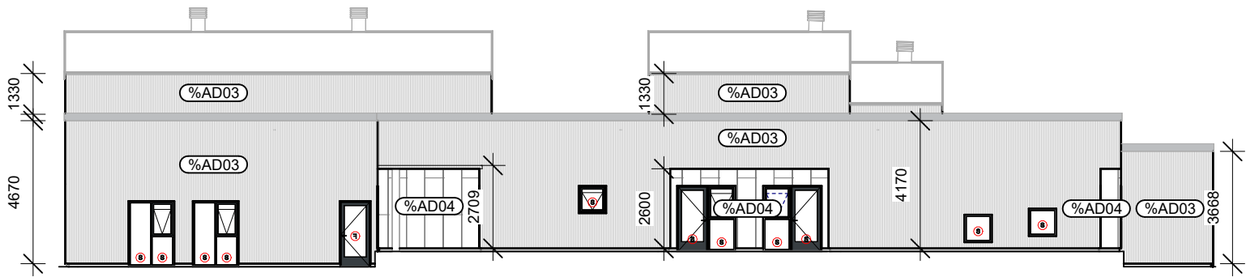

215 - Syd

Ny Daginstitution Smørum NDS_A6_K01_H2_EX_N01_S215

Udbudsprojekt

Opstalter

Mål: 1 : 200 Dato: 18.06.2026

TS-ARKITEKTER

Sags nr.: NDS Udarbejdet af: ST Kontrol af: TT Godk. af: TS Format: 297 x 420

TS-Arkitekter