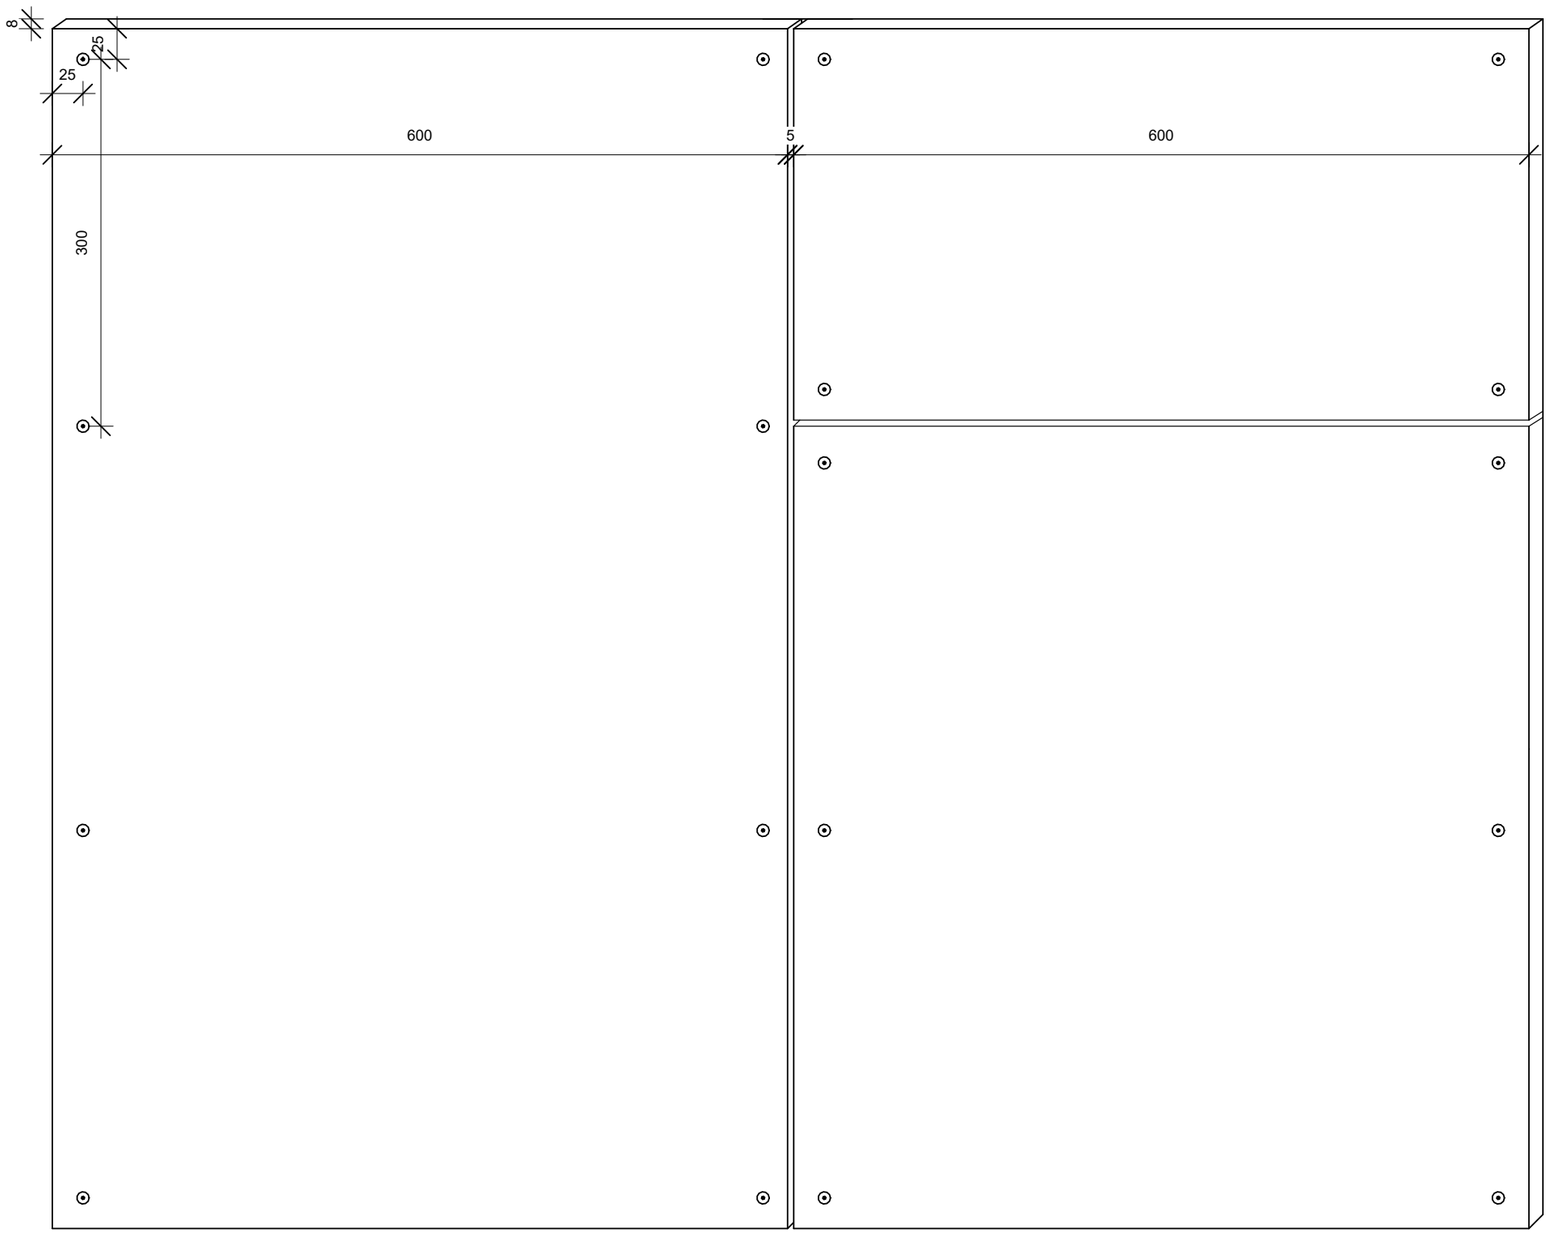


%AD04 Kompositbeklædning 8 mm

Kompositplade 8 mm
Brandklasse B-s1,d0
Lodrette stålprofiler c/c maks. 600 mm
Ventileret hulrum min. 50 mm
Ventilation i top og bund
Insektnet ved ventilationsåbninger
Hjørne- og afslutningsprofiler i aluminium
Fugeprofil mellem vandrette samlinger
Afslutninger iht. detailtegninger

Ny Daginstitution Smørum NDS_A6_K01_H1_N02_S215

Udbudsprojekt

%AD04 Kompositbeklædning

Mål: 1 : 5 Dato: 18.06.2026

TS-ARKITEKTER

Sags nr.: NDS Udarbejdet af: ST Kontrol af: TT Godk. af: TS Format: 297 x 420

TS-Arkitekter