
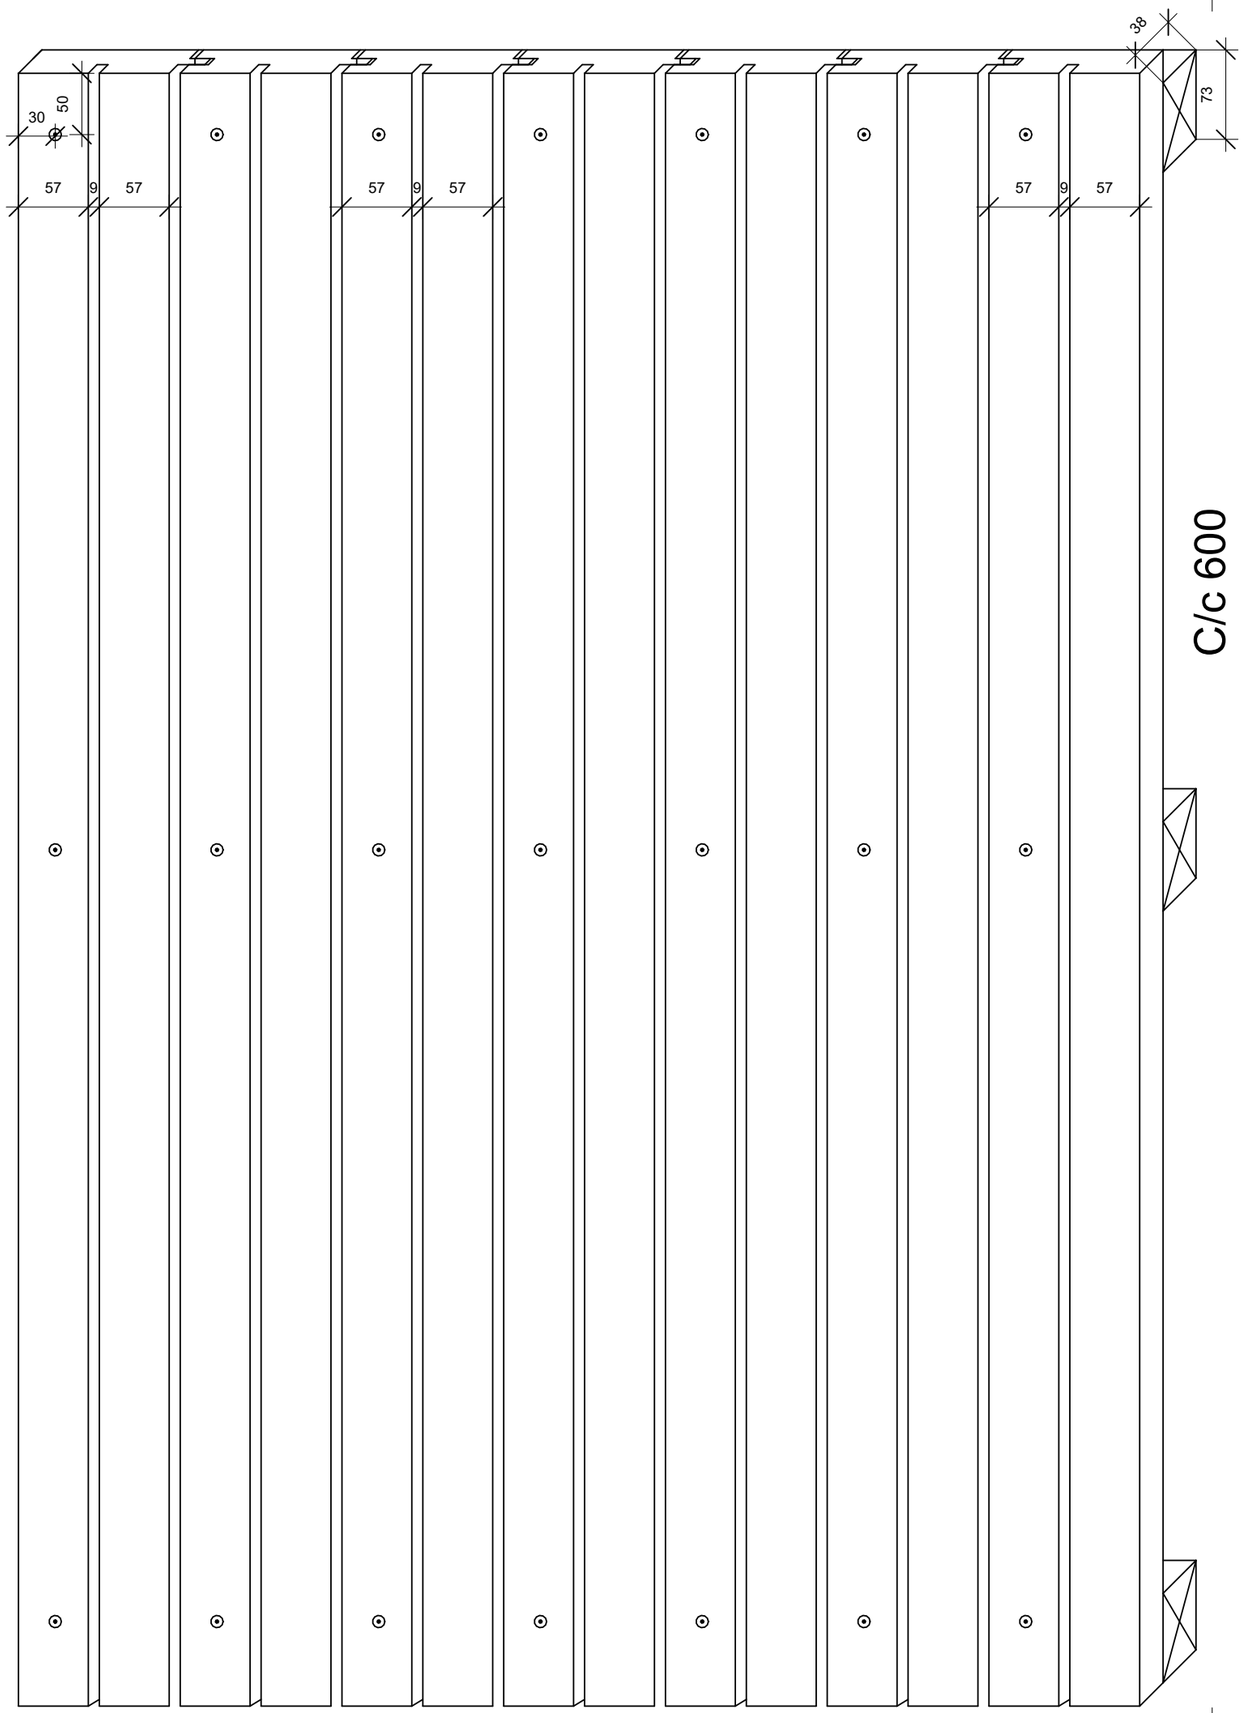


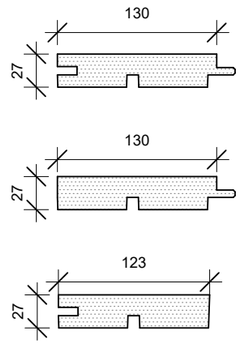

%AD03 Træbeklædning lodret 27 mm

Lodret træbeklædning af imprægneret grantræ.

Dimension: 27 × 145 mm
Dækbredde: 130 mm
Reaktion på brand: B-s2,d0 iht. EN 13501-1.

Beklædningen monteres på vandrette lægter 38 × 73 mm c/c maks. 600 mm.

Der skal sikres ventileret hulrum bag beklædningen med ventilationsåbninger i top og bund. Ventilationsåbninger forsynes med insektnet.

Beklædningen afsluttes min. 150 mm over færdigt terræn.

Hjørner, samlinger, afslutninger og tilslutninger udføres iht. detailtegninger.

Ny Daginstitution Smørum

NDS_A6_K01_H1_N01_S215

Udbudsprojekt

%AD03 Lodret Træbeklædning

Mål: 1 : 5 Dato: 18.06.2026

TS-ARKITEKTER

Sags nr.: NDS Udarbejdet af: ST Kontrol af: TT Godk. af: TS Format: 297 x 420

TS-Arkitekter