
**BYGNINGSDELSOVERSIGT**

| Typekode: | Beskrivelse |
|---|---|
| %AD02 | Ydervæg Isoleringslag 350 mm (0,13 W/m²K) (S215 Skeletkonstruktion)<br>Trykfast og vandafvisende mineraluld 150 mm<br>Trykfast og vandafvisende mineraluld 150 mm<br>Ventileret Stålforskalling 50 mm |
| %AD03 | Ydervæg Træbeklædning 65 mm (S215 Skeletkonstruktion)<br>Træbeklædning 160 mm lodret 27 mm<br>Ventileret Træforskalling 38 x 73 mm C/c 600 |
| %AD04 | Ydervæg Kompositbeklædning 46 mm (S215 Skeletkonstruktion)<br>Beklædning - Kompositplade 8 mm<br>Ventileret Træforskalling 38 x 73 mm C/c 600 |
| %AD05 | Letbeton Bagmur 150 mm (S210 Betonkonstruktion)<br>Letbetonelement 150 mm |

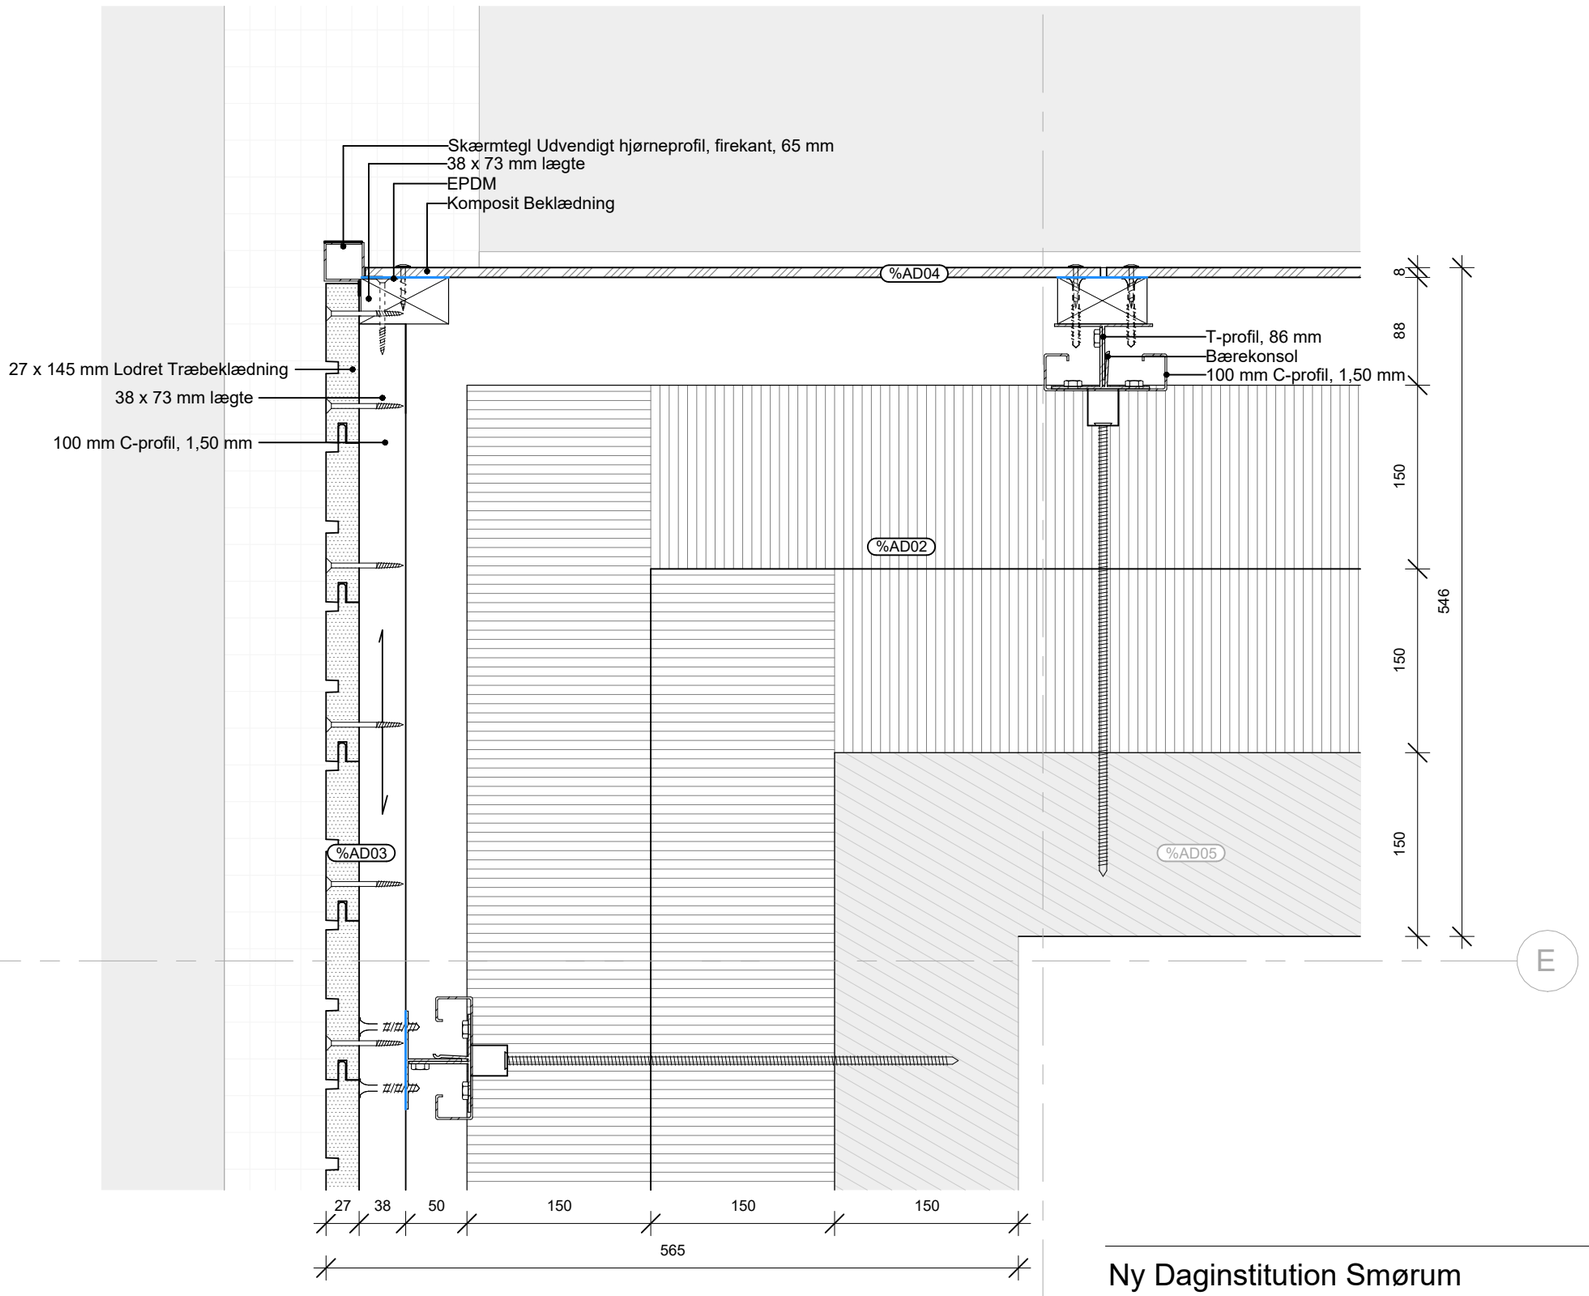


*Skruer iht. leverandørens anvisninger.

Ny Daginstitution Smørum NDS_A6_K01_H1_EST_N11_S215

Udbudsprojekt

V - Hjørnesamling (Komp/Træ)

Mål: 1 : 5 Dato: 18.06.2026

TS-ARKITEKTER

Sags nr.: NDS Udarbejdet af: ST Kontrol af: TT Godk. af: TS Format: 297 x 420

TS-Arkitekter