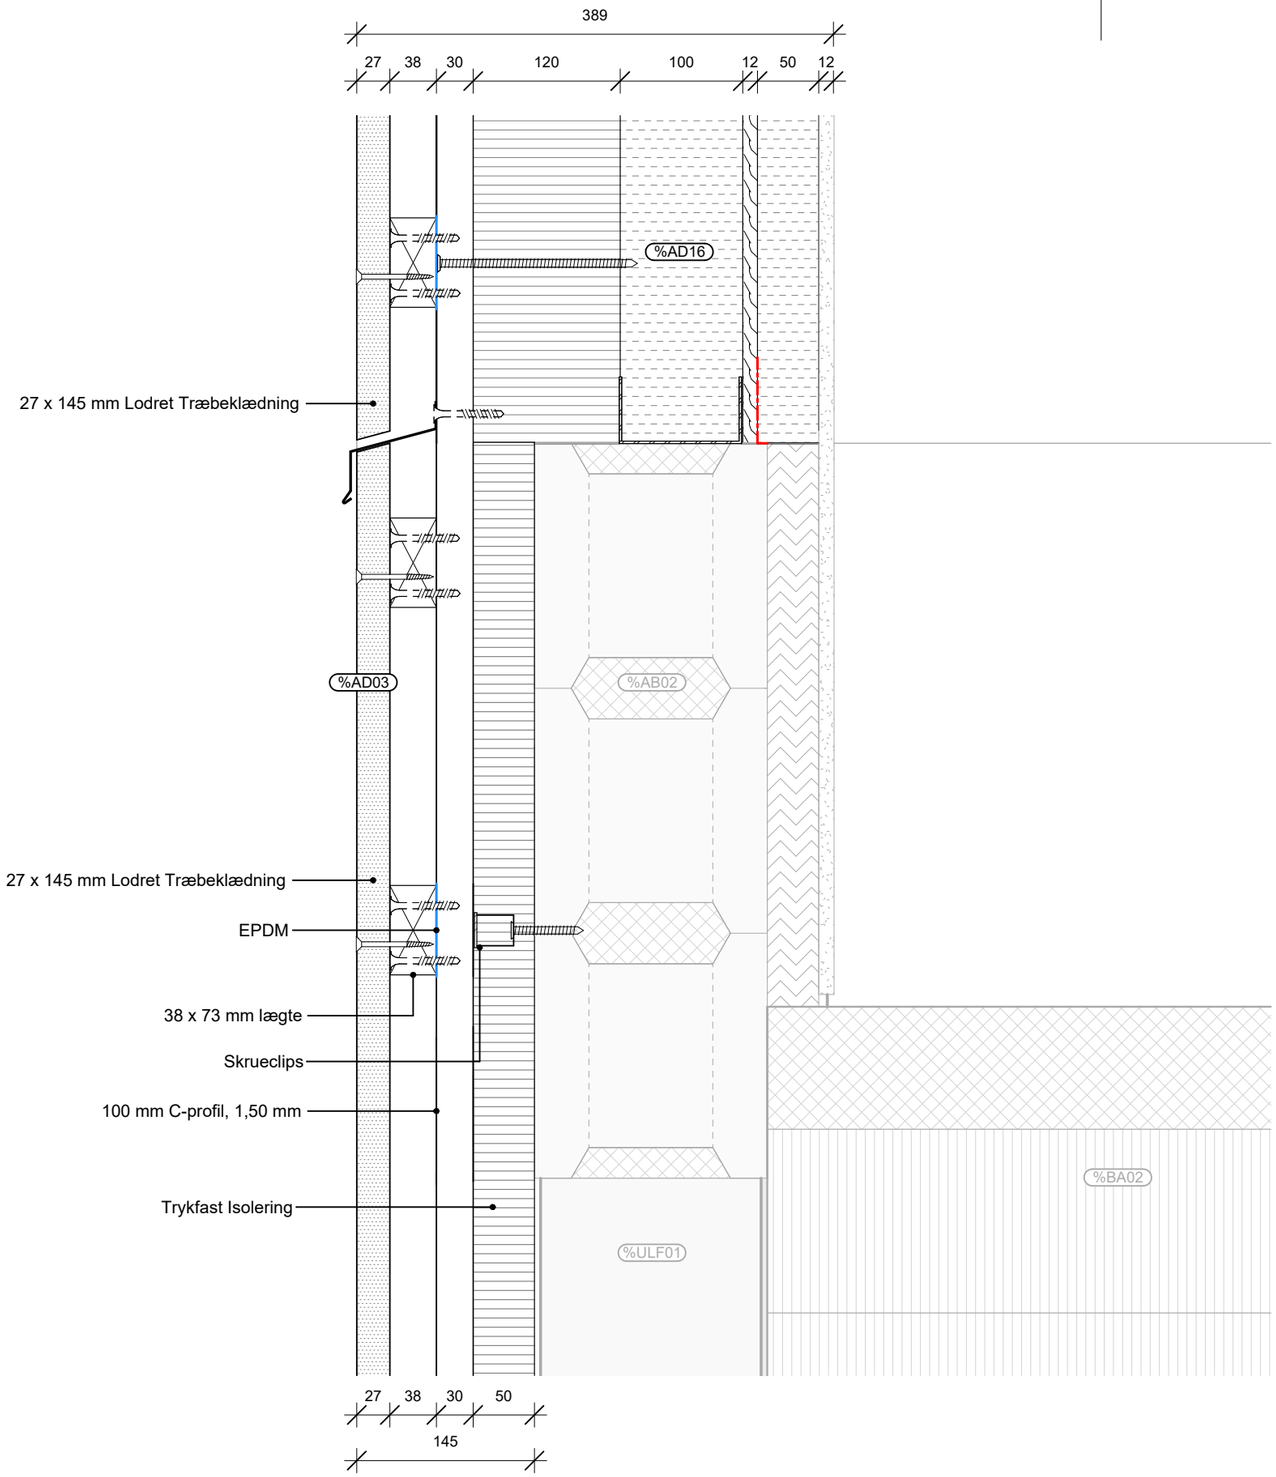


*Skruer iht. leverandørens anvisninger.

BYGNINGSDELSOVERSIGT

Typekode:	Beskrivelse
%AB02	Fundamentsblokke 190 mm (S201 Jord) Indstøbt Betonblokke Med Jern 190 mm
%AD03	Ydervæg Træbeklædning 65 mm (S215 Skeletkonstruktion) Træbeklædning 160 mm lodret 27 mm Ventileret Træforskalling 38 x 73 mm C/c 600
%AD16	Ydervæg Teknikrum 324 mm (0,13 W/m²K) (S215 Skeletkonstruktion) Ventileret Stålforskalling 30 mm Trykfast og vandafvisende mineraluld 120 mm Mineraluld 100 mm OSB 12 mm Installationslag C/c 600 mm 50 mm Fibergips 12 mm
%BA02	Teknikrum Gulvopbygning 400 mm (S225 Murer) Beton-in situ 100 mm Isolering Trykfast 150 mm Isolering Trykfast 150 mm
%ULF01	RB 180 x 230 mm (S210 Betonkonstruktion)

Ny Daginstitution Smørum NDS_A6_K01_H1_EST_N06_S215

Udbudsprojekt

L - Etageadskillelse

Mål: 1 : 5 Dato: 18.06.2026

TS-ARKITEKTER

Sags nr.: NDS Udarbejdet af: ST Kontrol af: TT Godk. af: TS Format: 297 x 420

TS-Arkitekter